

Access-Based Speed Limit Recommendation

MCL 257.627(2)(f)-(j): driveways and intersecting roadways count equally; see (18)(b).

Access points per 1/2 mile and the corresponding statutory speed:

Below 30 Not prescribed (2)(f)-(j)	30-39 45 mph (2)(j)	40-44 40 mph (2)(i)	45-49 35 mph (2)(h)	50-59 30 mph (2)(g)	60 or more 25 mph (2)(f)
--	---------------------------	---------------------------	---------------------------	---------------------------	--------------------------------

Method: sliding 2,640-ft (1/2-mile) windows, evaluated at access-entry/exit events and between events.

Most restrictive result: 35 mph at 0+04.36 - 26+44.36 (45 accesses).

Window Start	Window End	Length (ft)	Access Points	Recommended Speed	MCL 257.627 Basis
0+00	26+40	2,640	44	40 mph	(2)(i)
0+02.18	26+42.18	2,640	44	40 mph	(2)(i)
0+04.36	26+44.36	2,640	45	35 mph	(2)(h)
0+81.39	27+21.39	2,640	45	35 mph	(2)(h)
0+90.82	27+30.82	2,640	44	40 mph	(2)(i)
1+00.26	27+40.26	2,640	44	40 mph	(2)(i)

Sliding windows are the application method, not an explicit MCL requirement. The chart interval does not affect results.

Rows show endpoint windows, the peak count, and speed-category changes. Both window ends are included.

Different adjoining densities need separate determinations under (5)(b); the peak is not a limit for the whole alignment.

Special-area limits in (2)(a)-(e) may apply. Below 30, (2)(f)-(j) prescribe no speed; the 55-mph general limit in (9)

applies to trunk line and county highways only when no other limit is fixed. A filed order and posting are required (11)-(12).

A modified limit under MCL 257.628 supersedes the access-based result under (13). No partial-window extrapolation.

[MCL 257.627 - official statute](#)

[MCL 257.628 - modified speed limits](#)

Hypothetical Speed Limit Every 100 Feet


HYPOTHETICAL ONLY - independent 100-ft sections, scaled to half-mile density.

Equivalent half-mile count = section access count x 2,640 / section length in feet.

MCL 257.627(2)(f)-(j) supplies the comparison thresholds; it does not authorize this 100-ft method.


Each full section: 0-1 access = no category; 2 accesses = 30 mph; 3 or more = 25 mph.

The final partial section uses its actual length. This graph does not change the MCL recommendation.

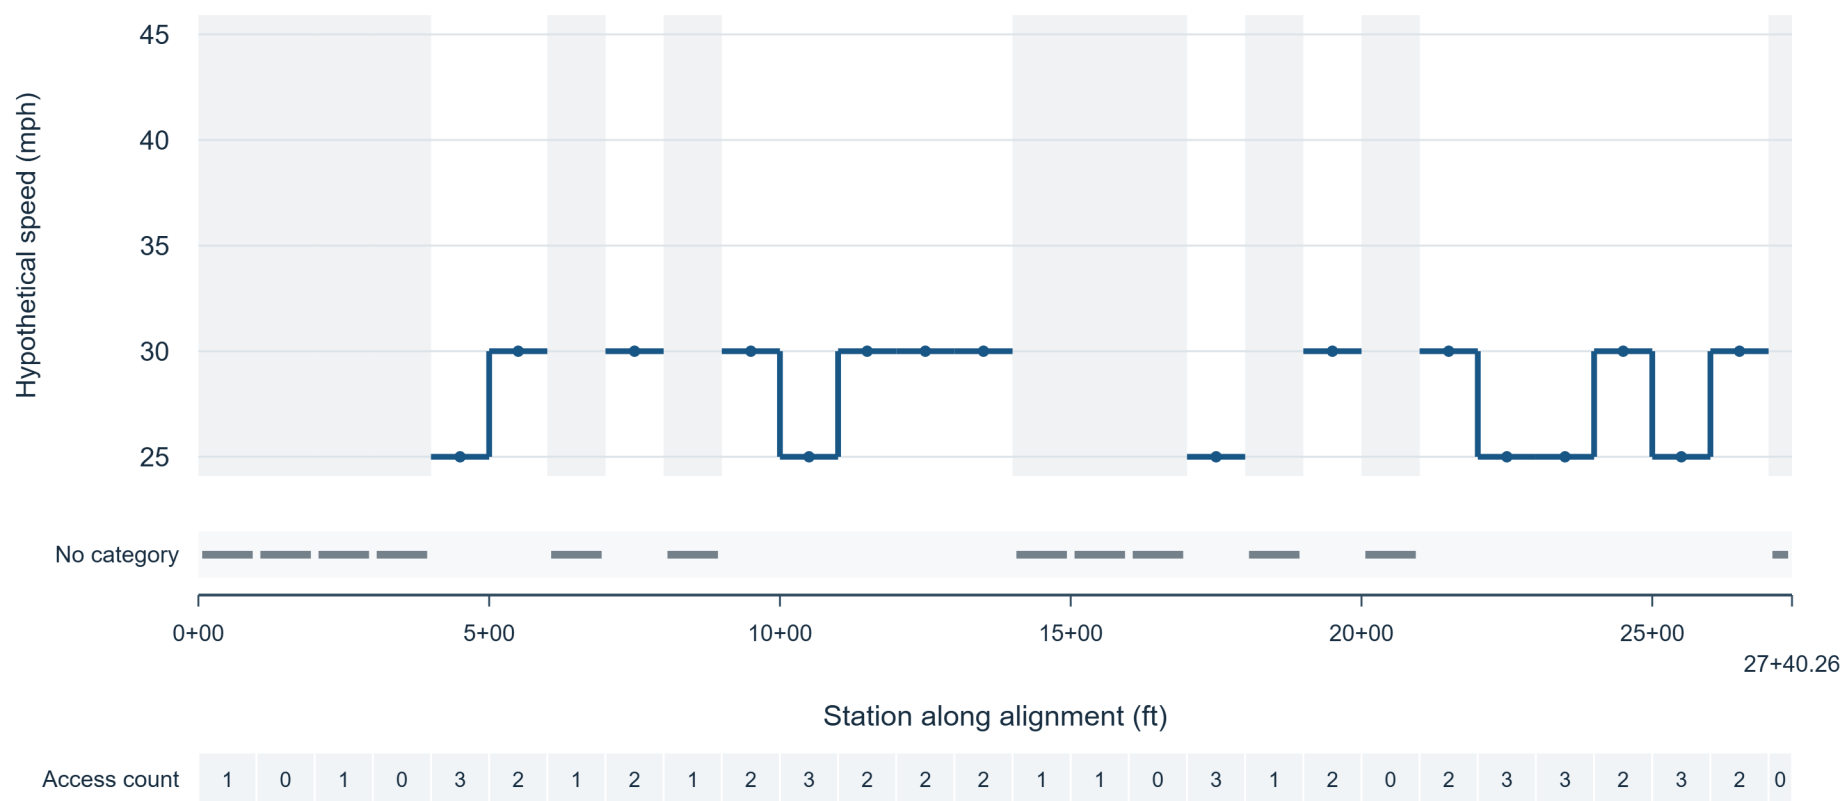


[MCL 257.627 - comparison thresholds only](#)

Access Point Density Along Alignment

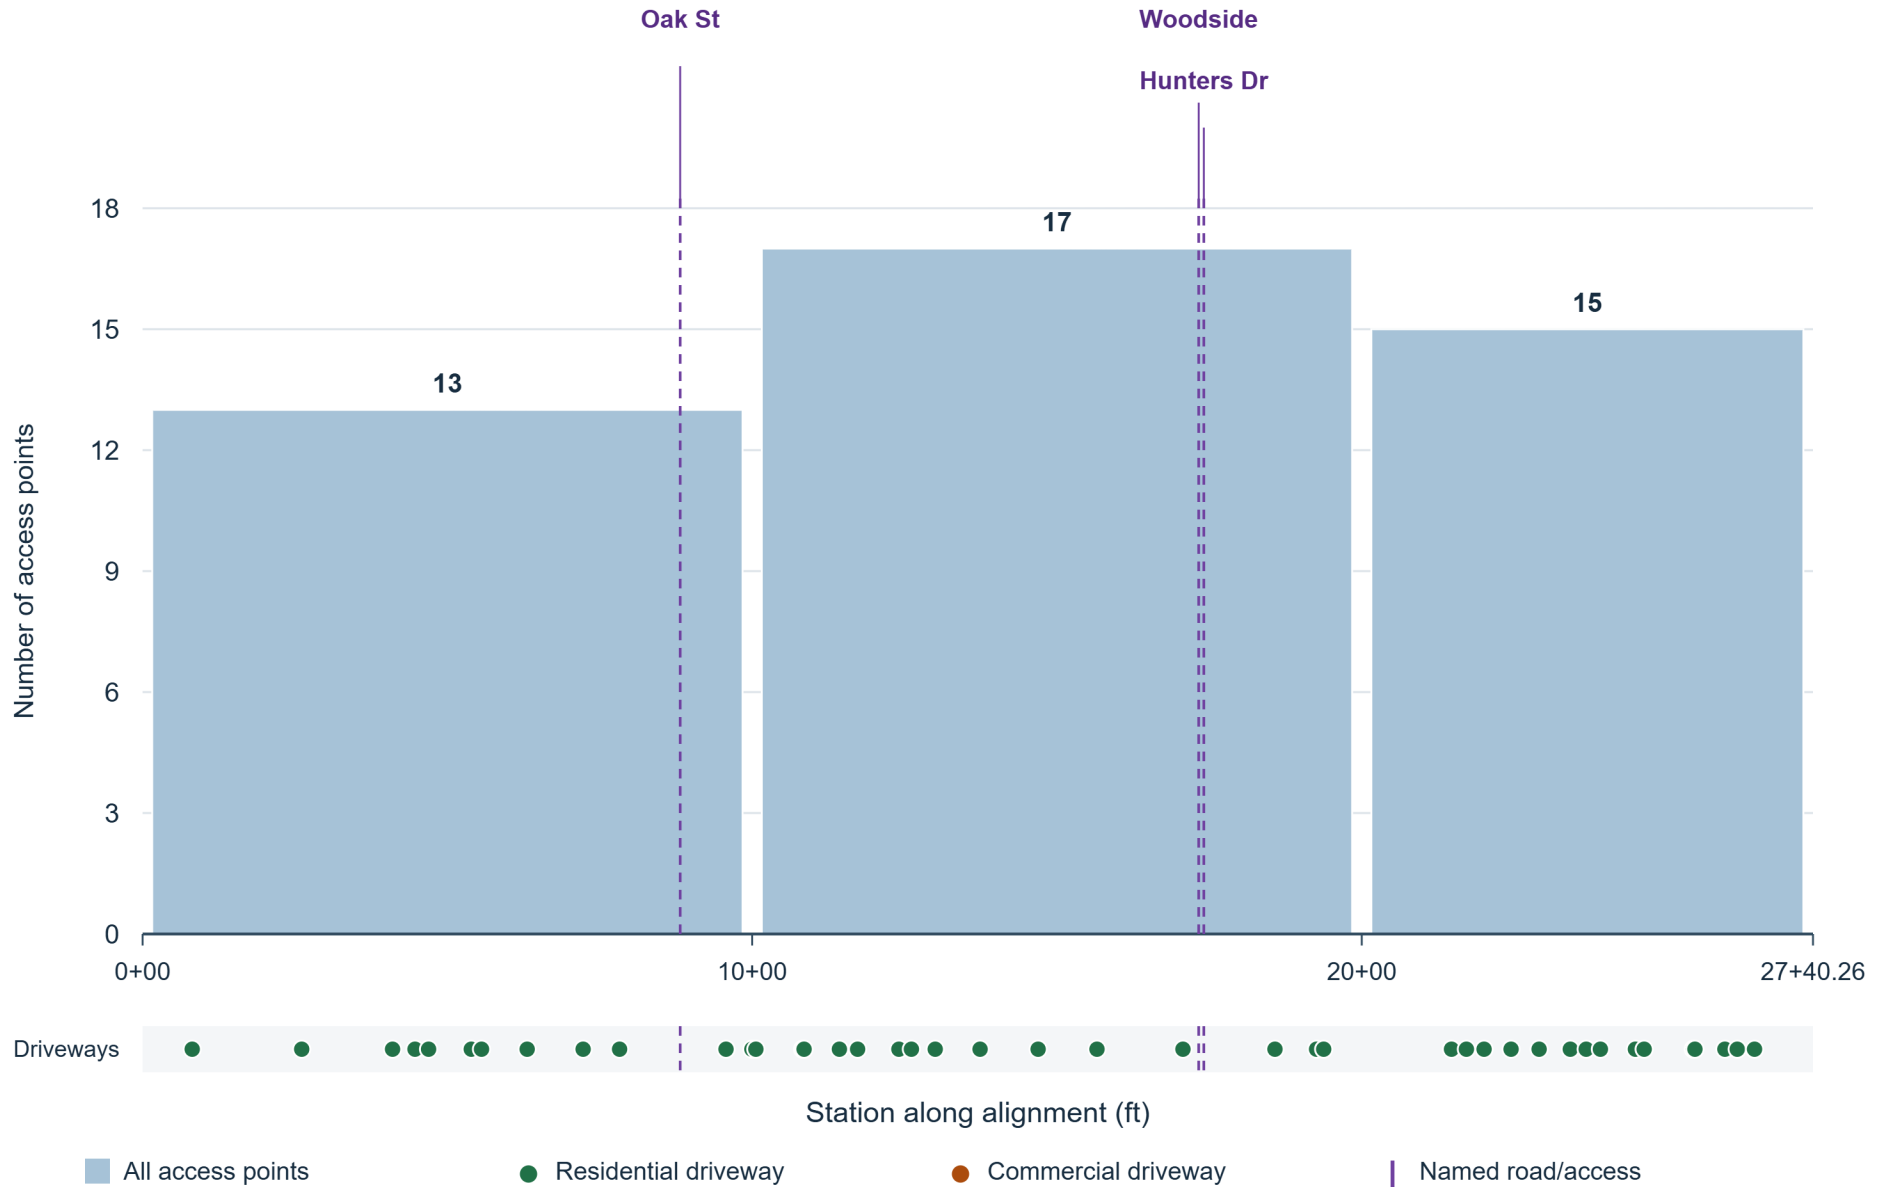


Stacked Access Type

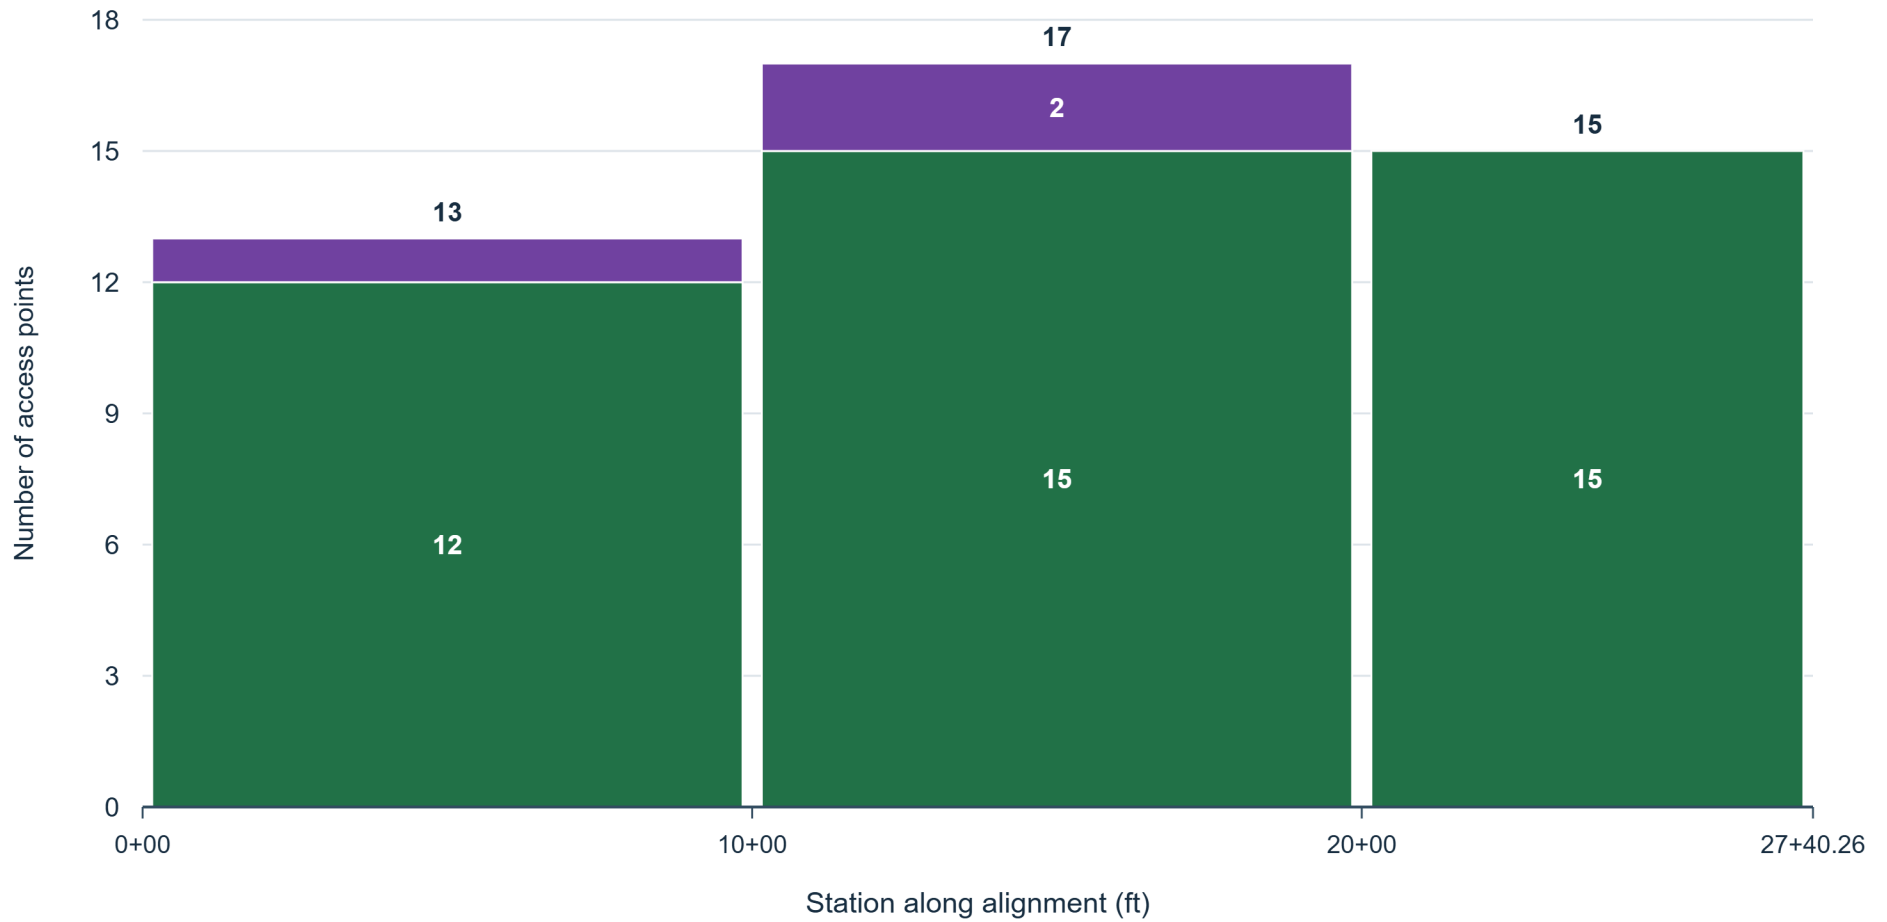

Residential driveway Commercial driveway Named road/access

Commercial / Named Access

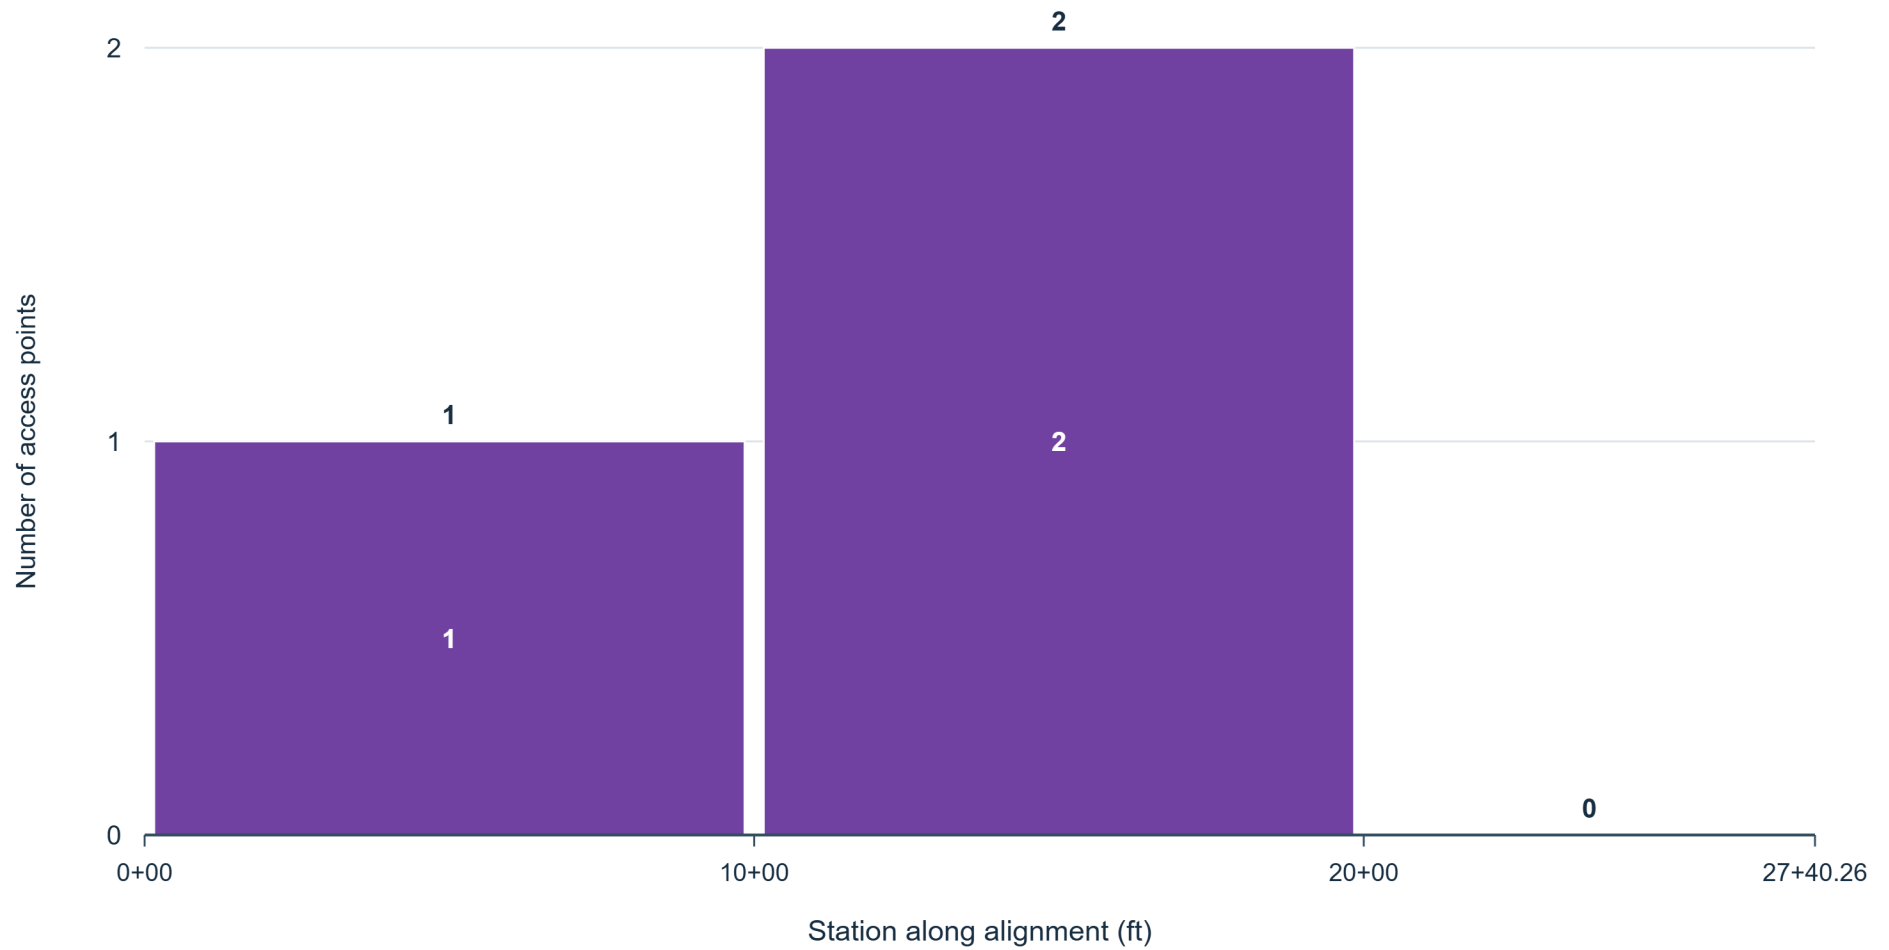

Commercial driveway Named road/access

Access Gaps

Start Station	End Station	Gap Length	Previous Access	Next Access
19+37.58	21+47.22	209.65 ft	Residential driveway	Residential driveway
0+81.39	2+61.02	179.64 ft	Residential driveway	Residential driveway
2+61.02	4+10.05	149.03 ft	Residential driveway	Residential driveway
15+65.64	17+06.69	141.05 ft	Residential driveway	Residential driveway
17+40.93	18+57.63	116.69 ft	Hunters Dr	Residential driveway
7+82.49	8+81.89	99.4 ft	Residential driveway	Oak St
14+69.08	15+65.64	96.56 ft	Residential driveway	Residential driveway
13+73.86	14+69.08	95.22 ft	Residential driveway	Residential driveway
6+30.87	7+22.68	91.81 ft	Residential driveway	Residential driveway
24+63.31	25+43.74	80.44 ft	Residential driveway	Residential driveway
10+06.07	10+82.58	76.52 ft	Residential driveway	Residential driveway
8+81.89	9+57.08	75.19 ft	Oak St	Residential driveway
5+56.00	6+30.87	74.87 ft	Residential driveway	Residential driveway
13+00.28	13+73.86	73.58 ft	Residential driveway	Residential driveway
4+69.17	5+39.18	70.02 ft	Residential driveway	Residential driveway

Access Gaps

Start Station	End Station	Gap Length	Previous Access	Next Access
18+57.63	19+25.88	68.25 ft	Residential driveway	Residential driveway
11+72.97	12+40.71	67.74 ft	Residential driveway	Residential driveway
7+22.68	7+82.49	59.8 ft	Residential driveway	Residential driveway
10+85.15	11+43.09	57.94 ft	Residential driveway	Residential driveway
23+91.50	24+48.93	57.43 ft	Residential driveway	Residential driveway
22+90.96	23+42.12	51.16 ft	Residential driveway	Residential driveway
25+46.58	25+95.72	49.14 ft	Residential driveway	Residential driveway
22+44.95	22+90.96	46.01 ft	Residential driveway	Residential driveway
22+00.67	22+44.95	44.28 ft	Residential driveway	Residential driveway
9+57.08	9+99.54	42.46 ft	Residential driveway	Residential driveway
12+61.21	13+00.28	39.08 ft	Residential driveway	Residential driveway
4+10.05	4+46.89	36.84 ft	Residential driveway	Residential driveway
11+43.09	11+72.97	29.88 ft	Residential driveway	Residential driveway
21+71.66	22+00.67	29.01 ft	Residential driveway	Residential driveway
26+15.97	26+44.36	28.39 ft	Residential driveway	Residential driveway

Access Gaps

Start Station	End Station	Gap Length	Previous Access	Next Access
23+42.12	23+68.19	26.07 ft	Residential driveway	Residential driveway
17+06.69	17+32.51	25.82 ft	Residential driveway	Woodside
21+47.22	21+71.66	24.43 ft	Residential driveway	Residential driveway
23+68.19	23+91.50	23.31 ft	Residential driveway	Residential driveway
4+46.89	4+69.17	22.27 ft	Residential driveway	Residential driveway
12+40.71	12+61.21	20.5 ft	Residential driveway	Residential driveway
25+95.72	26+15.97	20.26 ft	Residential driveway	Residential driveway
5+39.18	5+56.00	16.82 ft	Residential driveway	Residential driveway
24+48.93	24+63.31	14.38 ft	Residential driveway	Residential driveway
19+25.88	19+37.58	11.7 ft	Residential driveway	Residential driveway
17+32.51	17+40.93	8.42 ft	Woodside	Hunters Dr
9+99.54	10+06.07	6.53 ft	Residential driveway	Residential driveway
25+43.74	25+46.58	2.83 ft	Residential driveway	Residential driveway
10+82.58	10+85.15	2.57 ft	Residential driveway	Residential driveway